
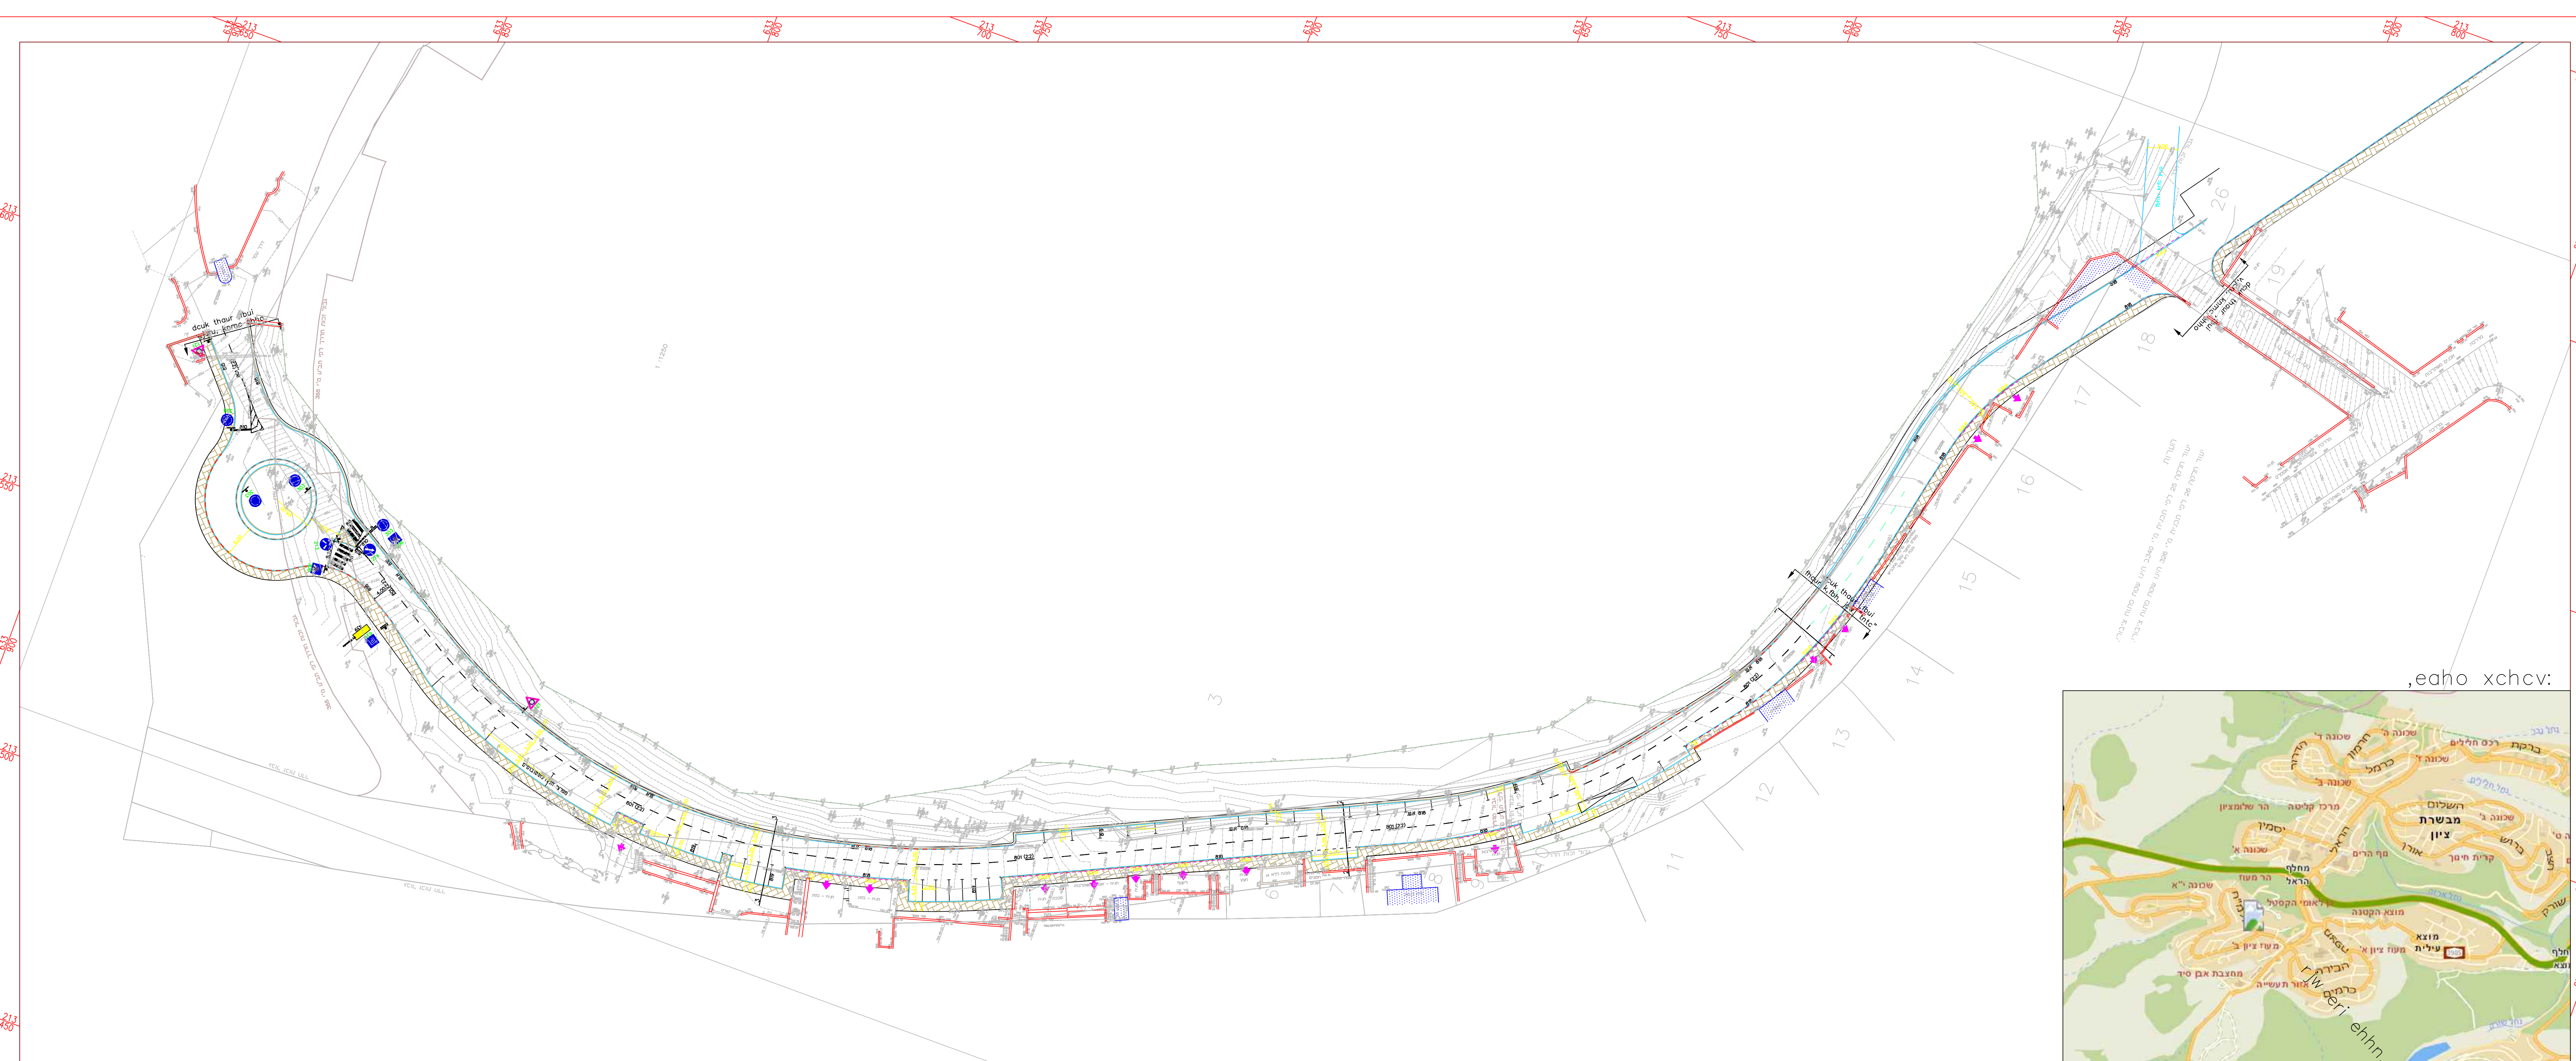
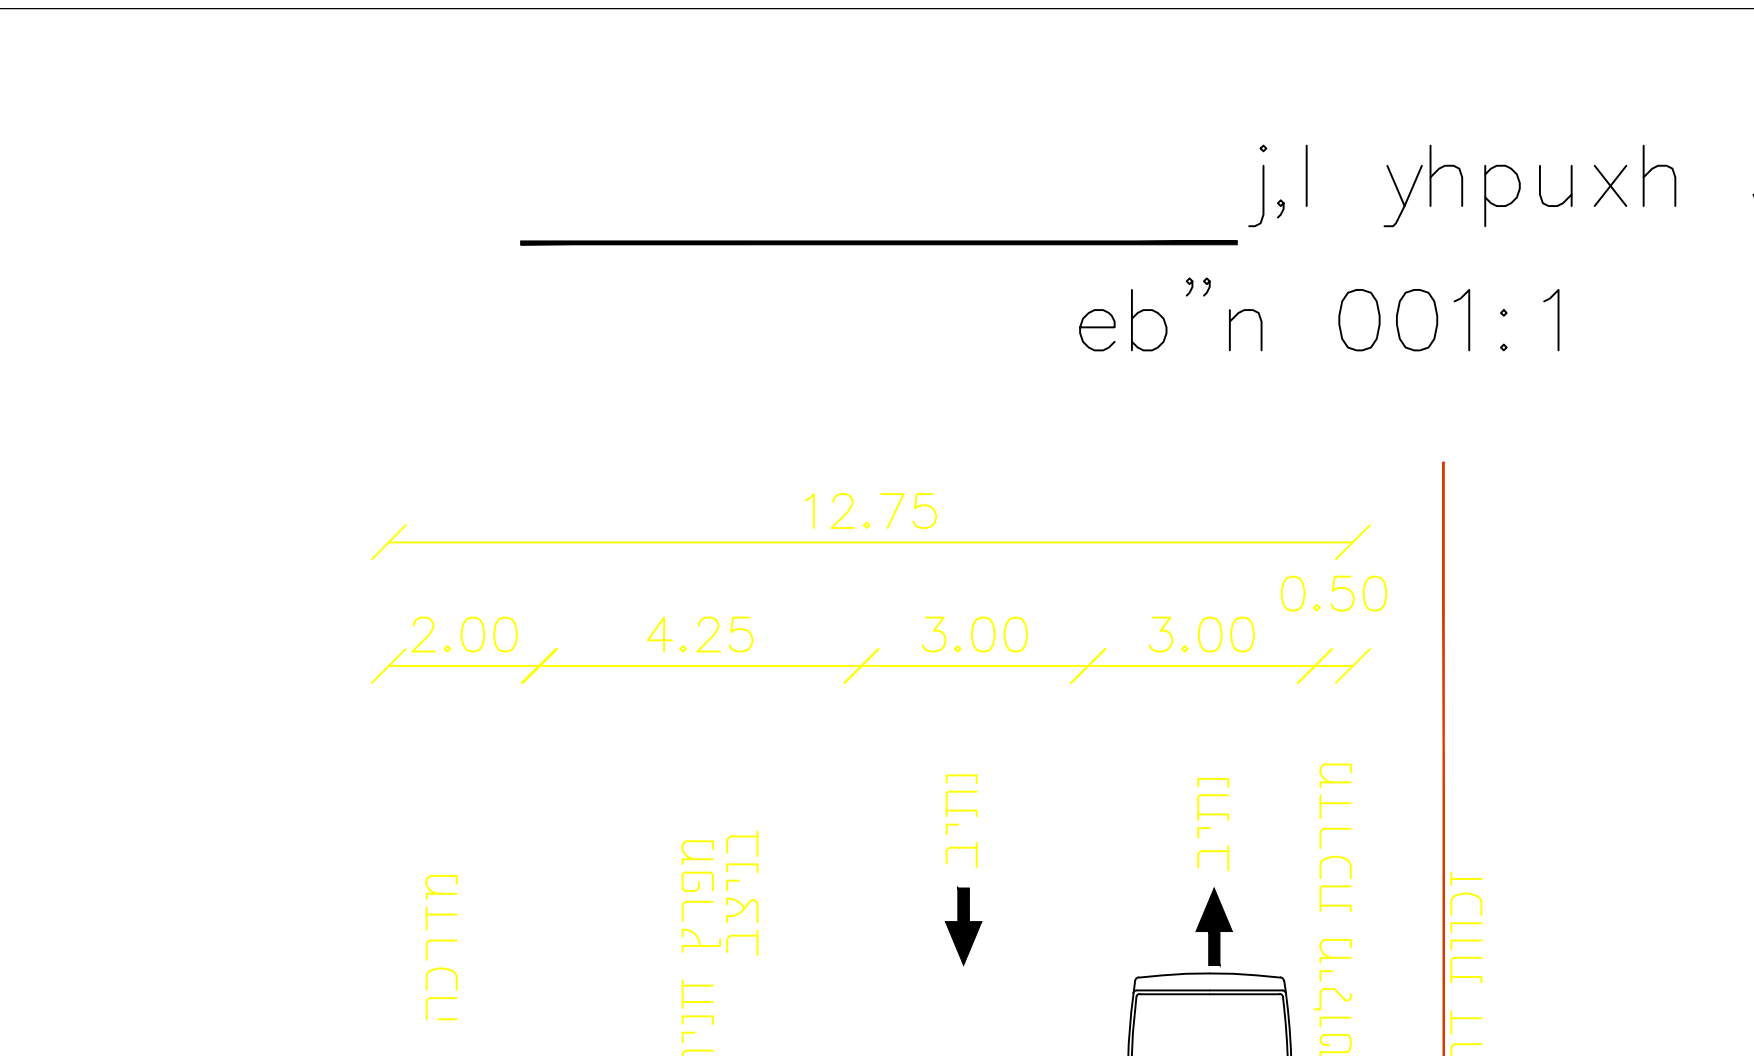
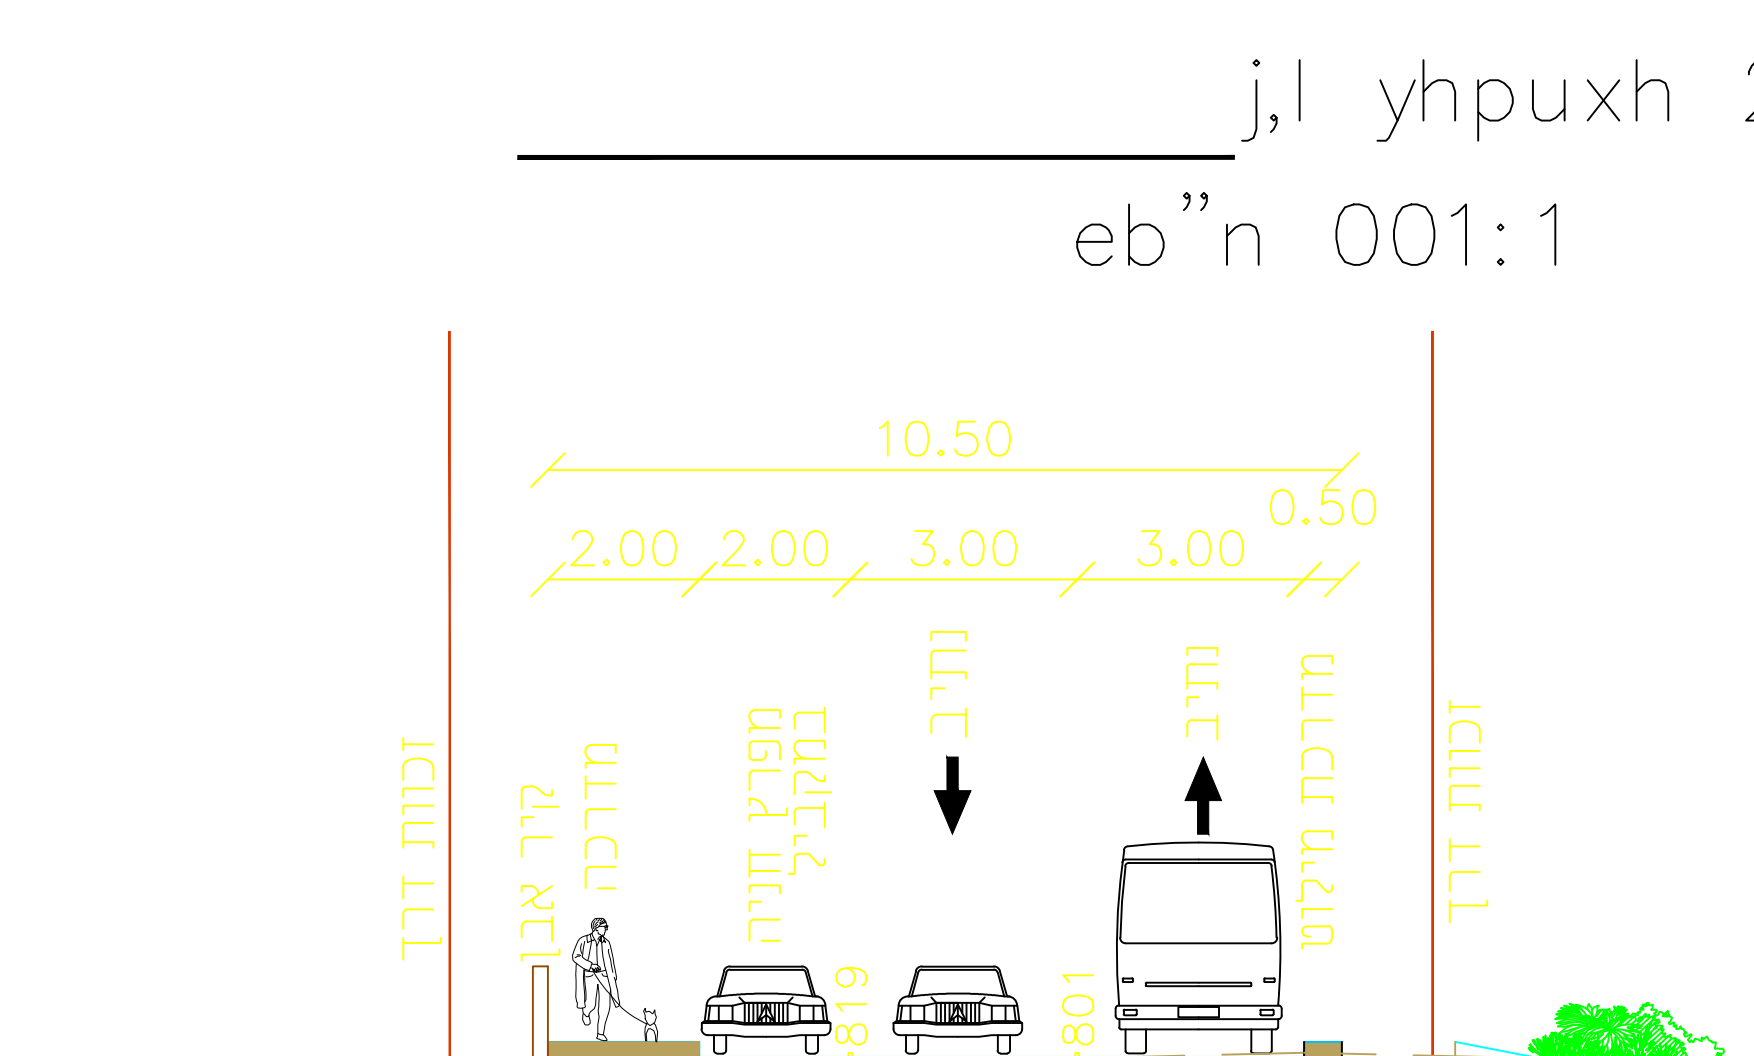


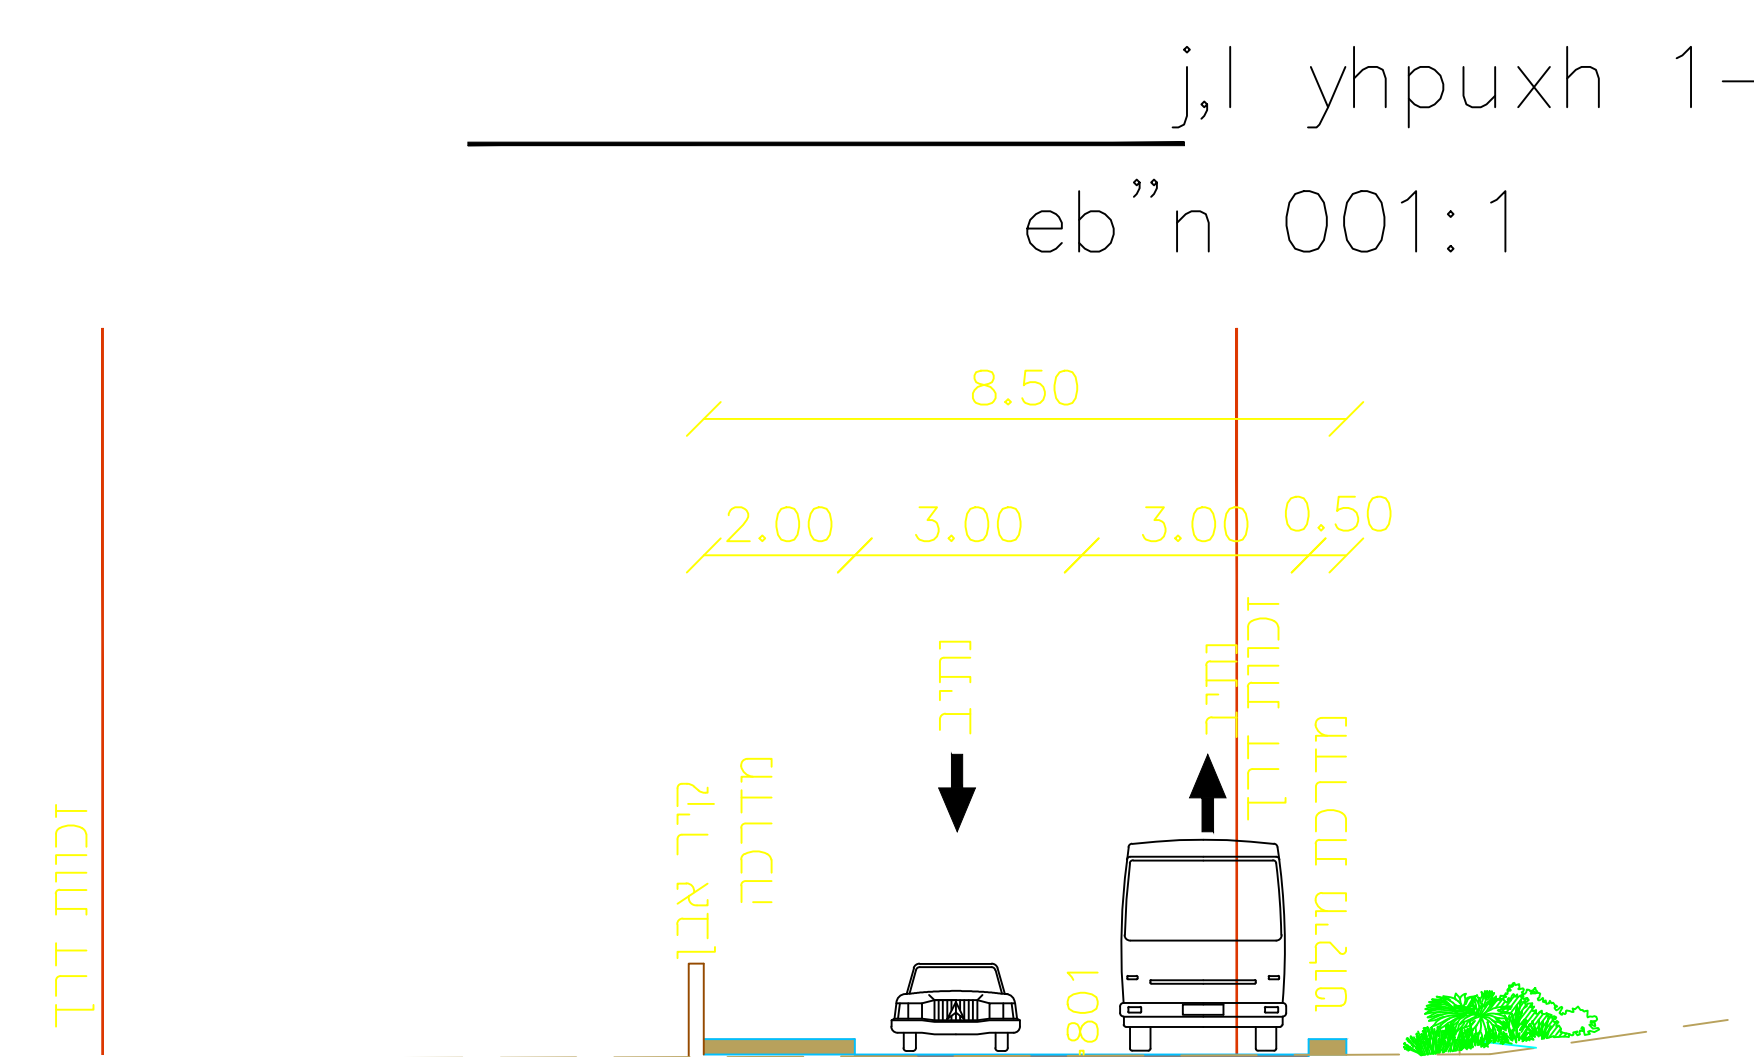

מקרא:

גבול זכות הדרך

עצים לעקירה העתקה
ייבדק בזמן תכנון מפורט

אבן שפה מתכננת